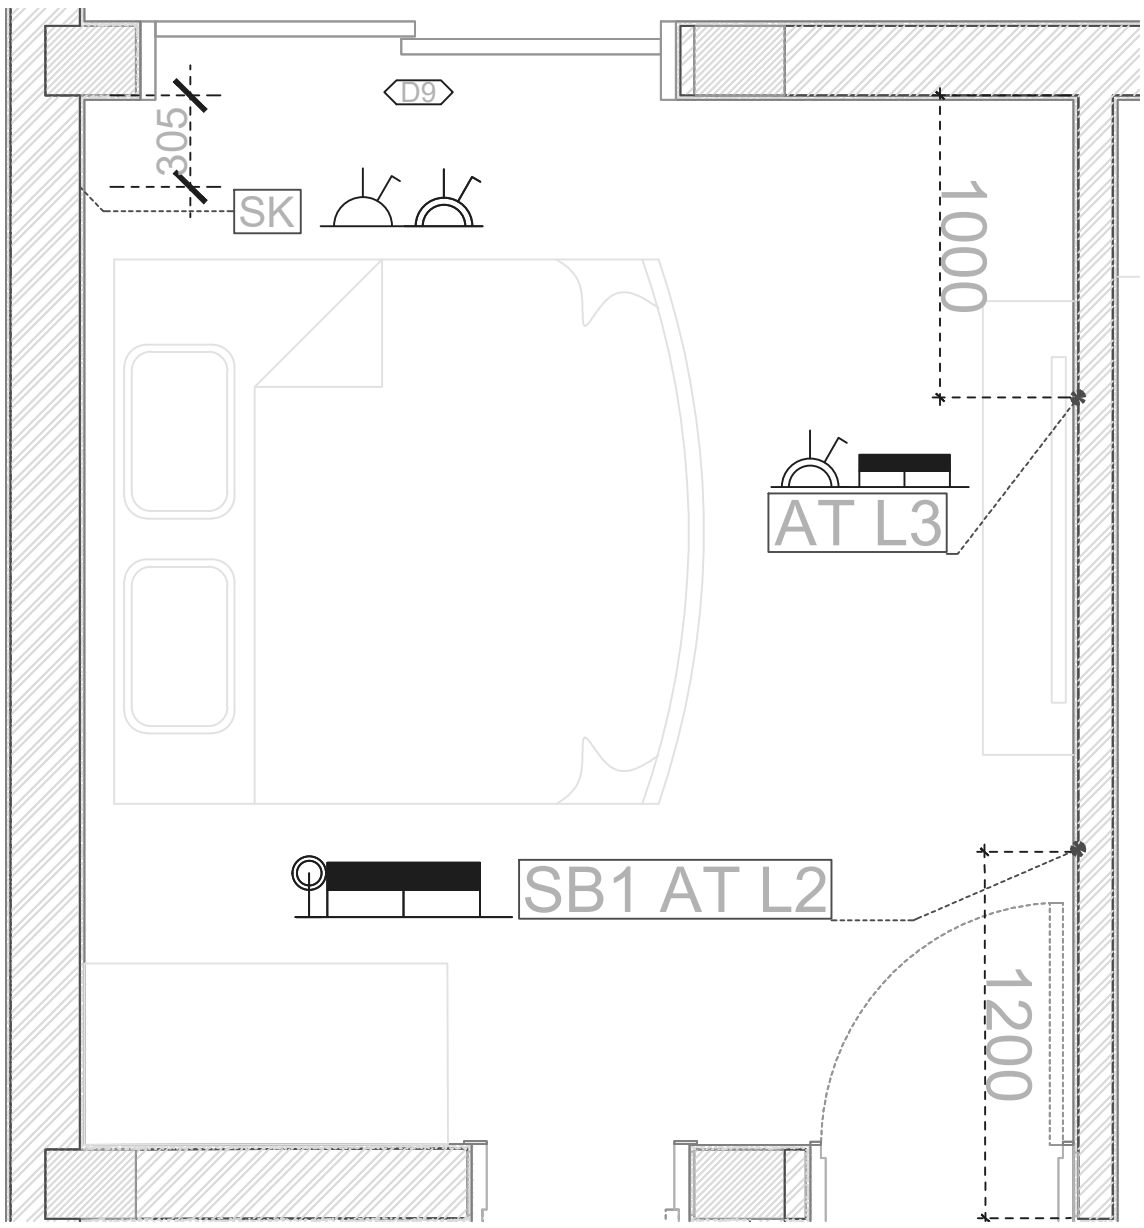

3 Electrical Layout
1:25

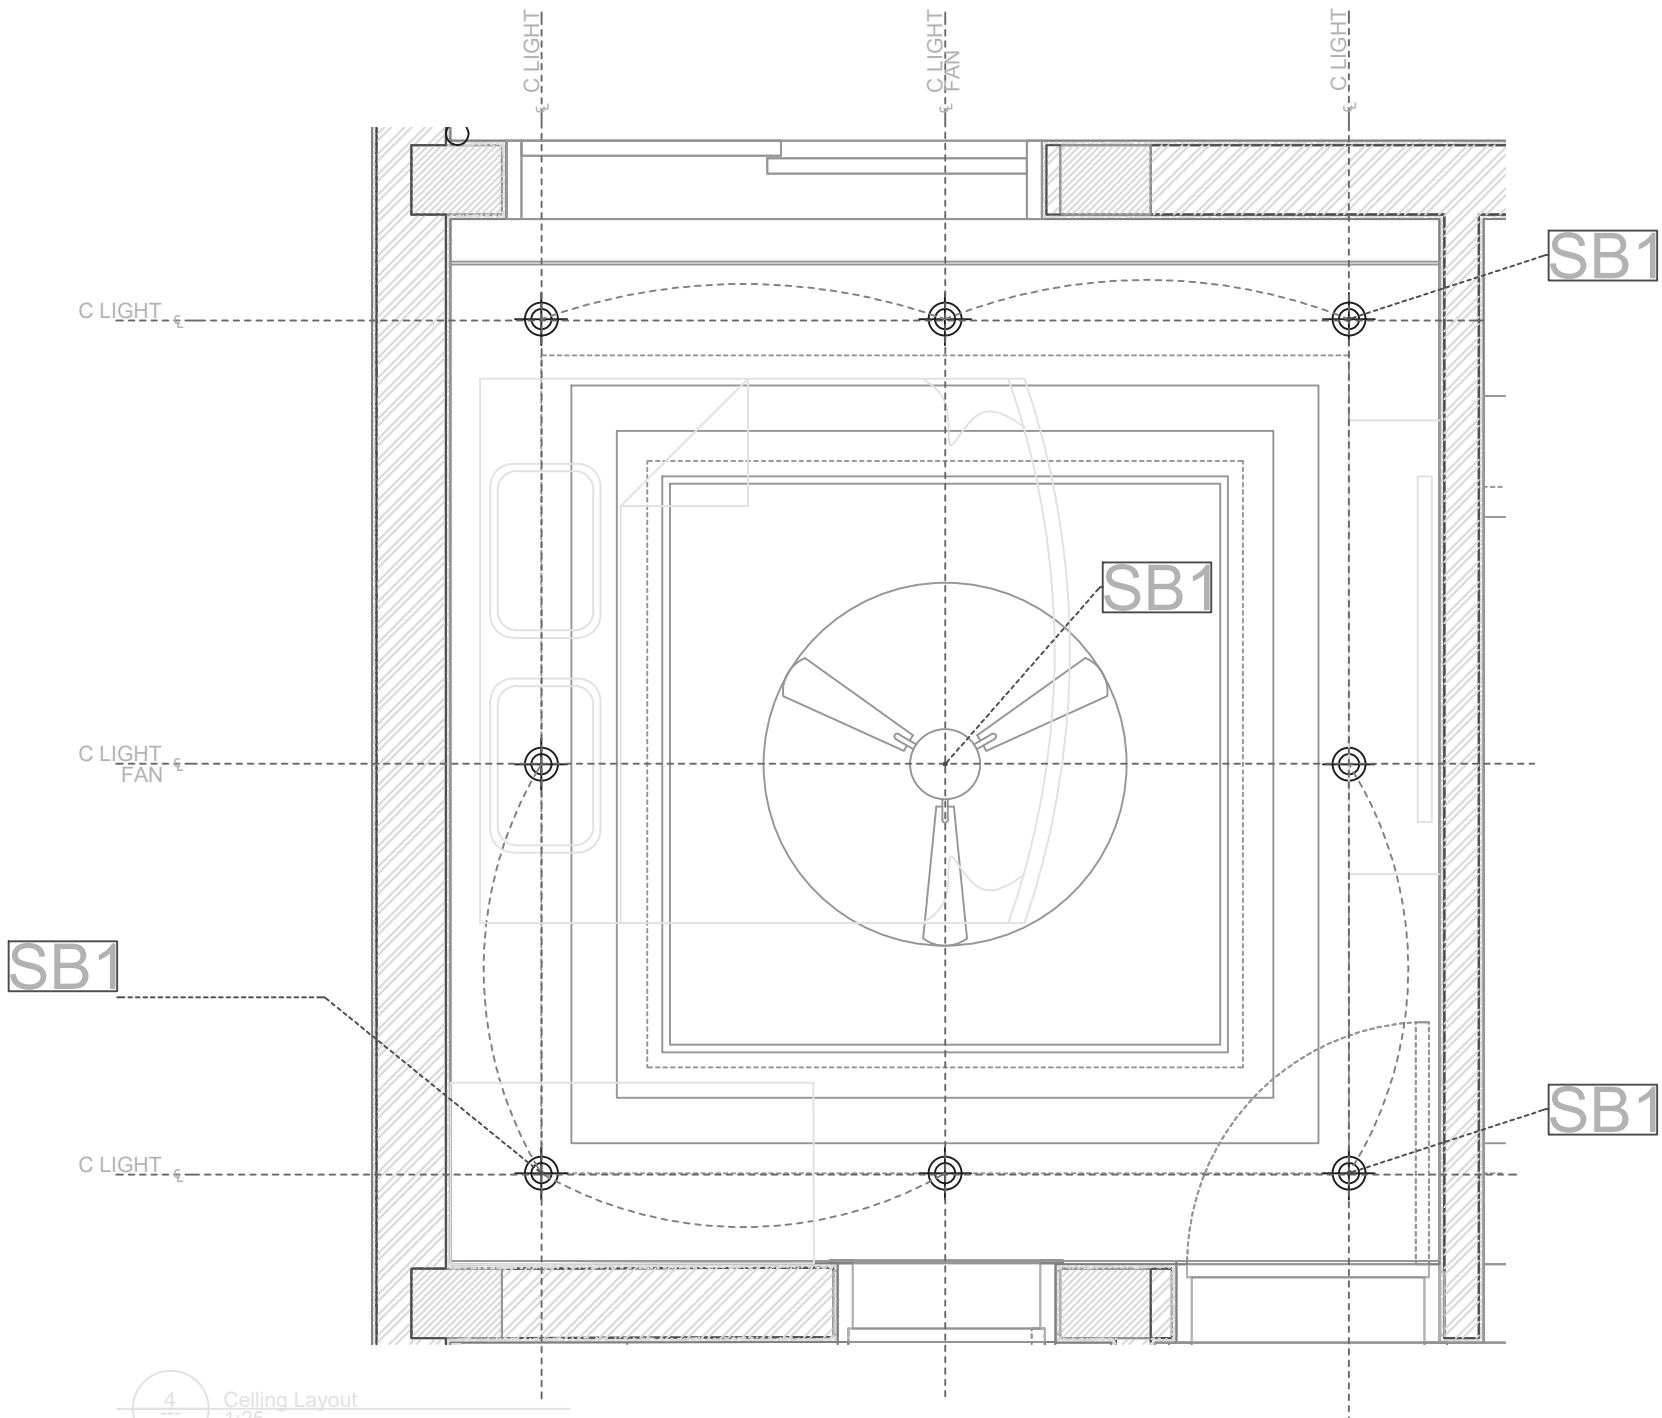

4 Celling Layout
1:25

KEY PLAN

DWG NO.

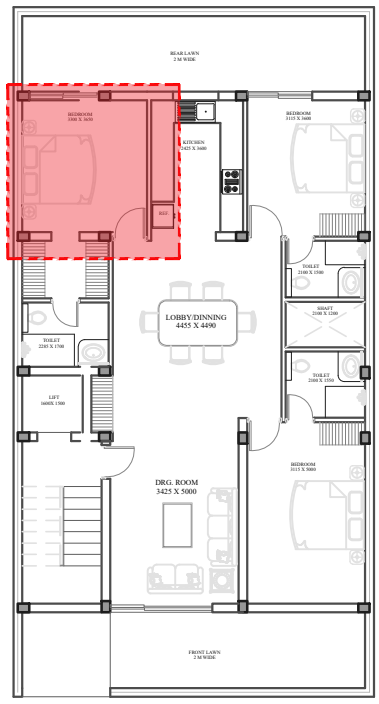

NOTES:

PROJECT

MASTER BEDROOM

CLIENT

MR. ASHOK SANGWAN

ONLY INFORMATION	○
EXISTING DWG	○
COMPLETION DWG.	○
PROPOSAL DWG.	○
SUBMISSION DWG.	○
TENDER DWG.	○
CONSTRUCTION DWG.	○
SCALE	NTS

DRAWN BY -

CHECKED BY-

REV.NO

DATE:
06-10-2025

ELECTRICAL DRAWING

OFFICE ADDRESS:
SOLACE STUDIO
HOUSE NO. 114 , AVENUE49 ,
SECTOR-49 , Gurgaon. 122018
Mobile : +91 9999 77 0200
Email : studiosolace.arch@gmail.com

SOLACE
STUDIO